



REV	DESCRIPTION	DATE	BY
P2	Concept sheet	2026-10-02	AC

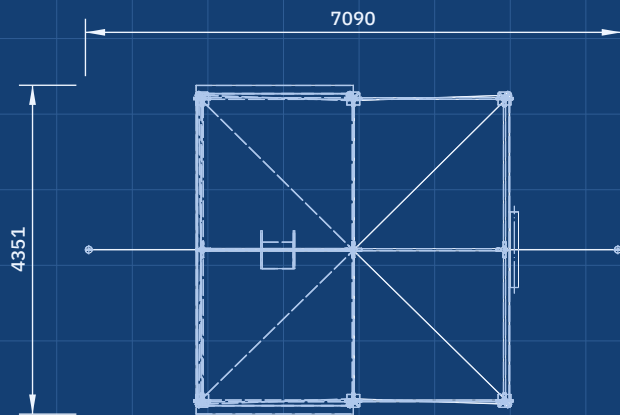


TOP VIEW

Scale 1:100; looking down (along -Z)

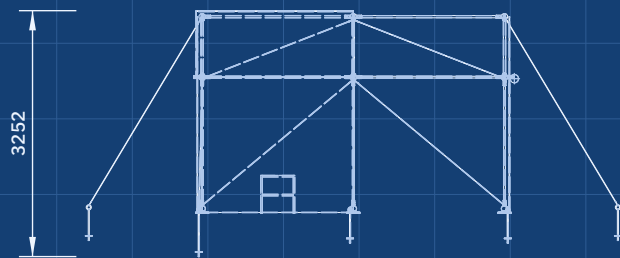


FRONT VIEW

Scale 1:100; looking at the front (along +Y)

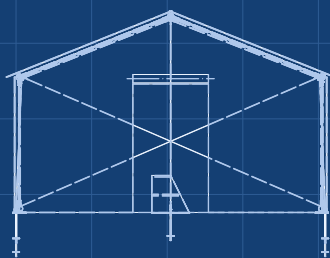

RIGHT VIEW

Scale 1:100; looking at the right side (along -X)

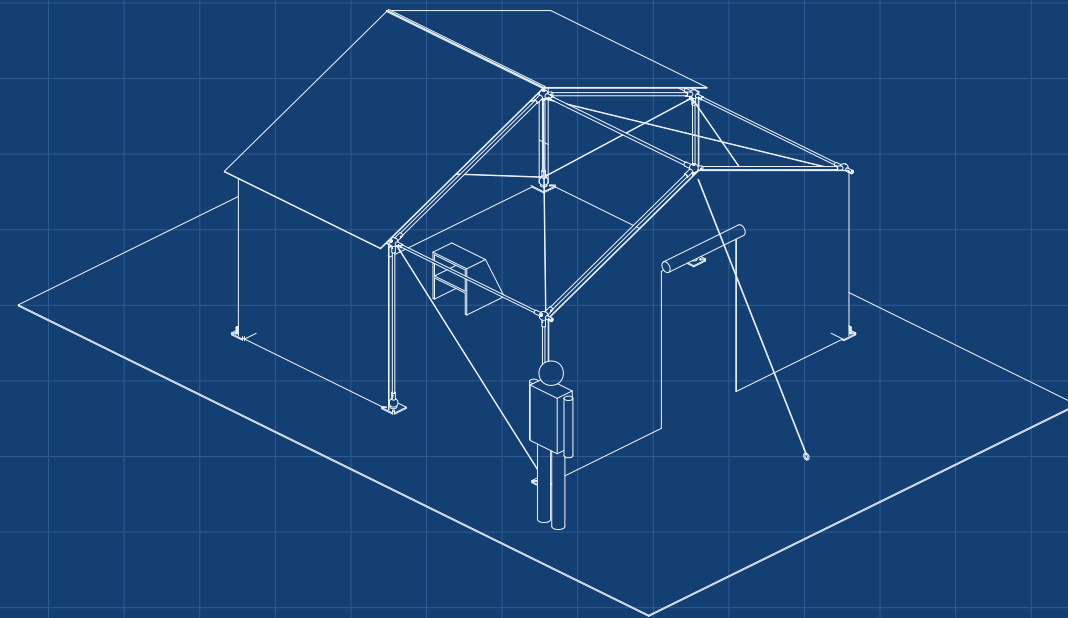

ISOMETRIC VIEW

Not to scale; grey is for scale; seen from the front right and above, about 30 deg elevation

KEY FIGURES

- Size M: 4.0 x 4.0 m floor (16 m²), eave 1.8 m, ridge 2.6 m
- 18 EMT members: 1 in rafters and ridge, 3/4 in posts and eaves
- 15 printed nodes in 4 variants (filled PA12-class nylon), no tools; folding step in the kit
- Frame kit 46.2 kg, \$701 (value-engineering target \$445)
- Wind rating 19.5 m/s, 3/4 in post governs (SNF-CAL-001 v0.6)

SNAPFRAME

github.com/BoujeeEnjinia1701/snapframe

Emergency shelter frame kit concept, size M

DRAWING NO. SNF-DWG-010	REV P2	SHEET 1 of 1	SIZE ANSI B
-----------------------------------	------------------	------------------------	-----------------------

SCALE 1:100	UNITS mm	PROJECTION 	DATE 2026-10-02	DRAWN Amish Chadha
-----------------------	--------------------	---	---------------------------	------------------------------

MATERIAL / NOTES Massing model for concept communication
--