
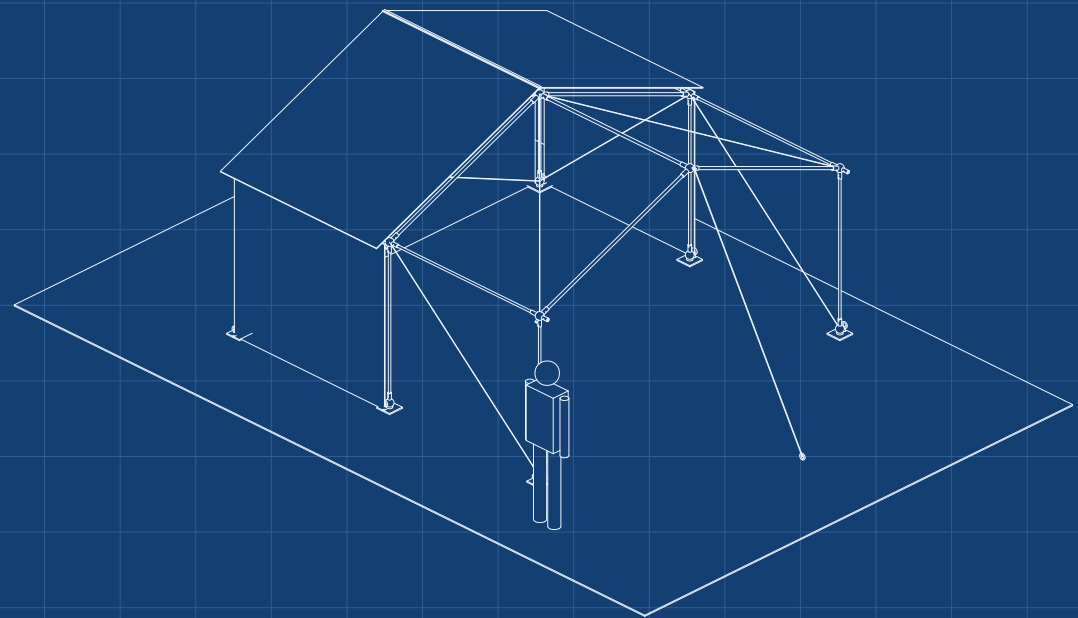
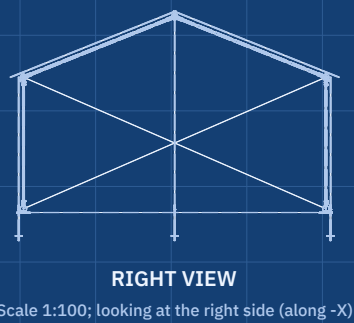
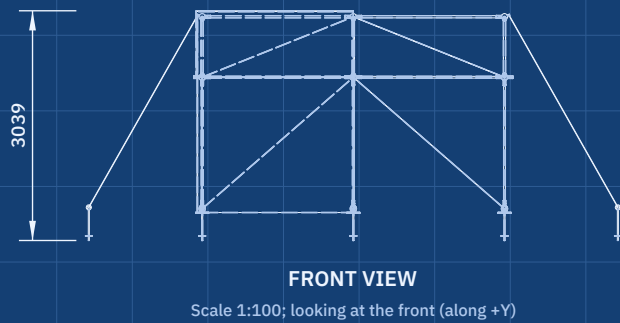


REV	DESCRIPTION	DATE	BY
P1	Concept sheet	2026-09-25	AC

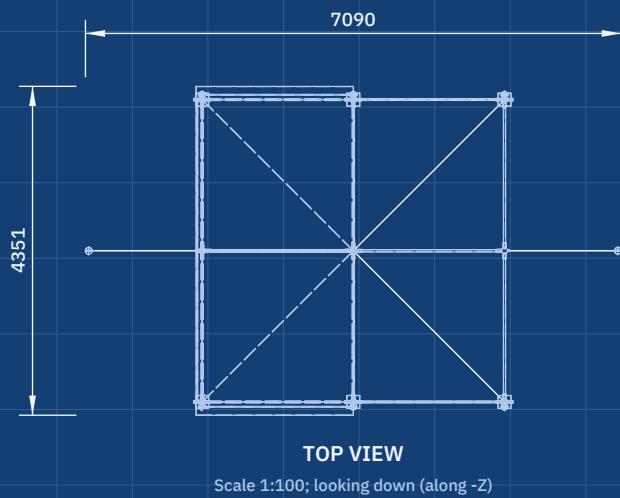

KEY FIGURES

Size M: 4.0 x 4.0 m floor (16 m²), eave 1.8 m, ridge 2.6 m
18 EMT members: 1 in rafters and ridge, 3/4 in posts and eaves
15 printed nodes in 4 variants, spring-button sockets, no tools
Frame kit 42.0 kg, \$443 (budget \$445); tarpaulins agency stock
Wind rating 19.7 m/s, 3/4 in post governs (SNF-CAL-001)

SNAPFRAME

github.com/BoujeeEnjinia1701/snapframe

Emergency shelter frame kit concept, size M

DRAWING NO. SNF-DWG-010		REV P1	SHEET 1 of 1	SIZE ANSI B
SCALE 1:100	UNITS mm	PROJECTION 	DATE 2026-09-25	DRAWN Amish Chadha
MATERIAL / NOTES Massing model for concept communication				
Licensed CERN-OHL-S-2.0 · Design Molecule Lab · designmolecule.com				Generated from cad/src; do not edit by hand