



CONCEPT, NOT FOR FABRICATION


REV	DESCRIPTION	DATE	BY
P1	Concept sheet	2026-09-25	AC

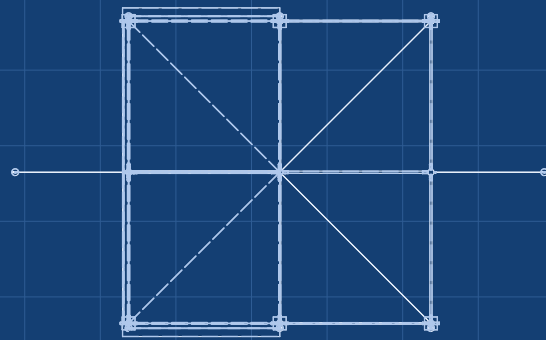


TOP VIEW
Scale 1:100

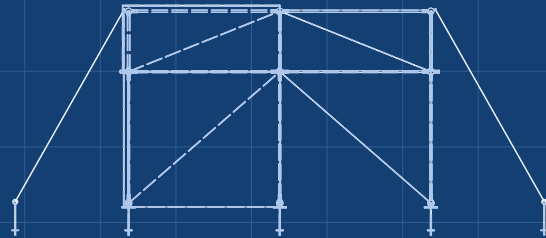

FRONT VIEW
Scale 1:100

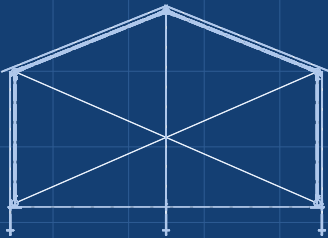

RIGHT VIEW
Scale 1:100

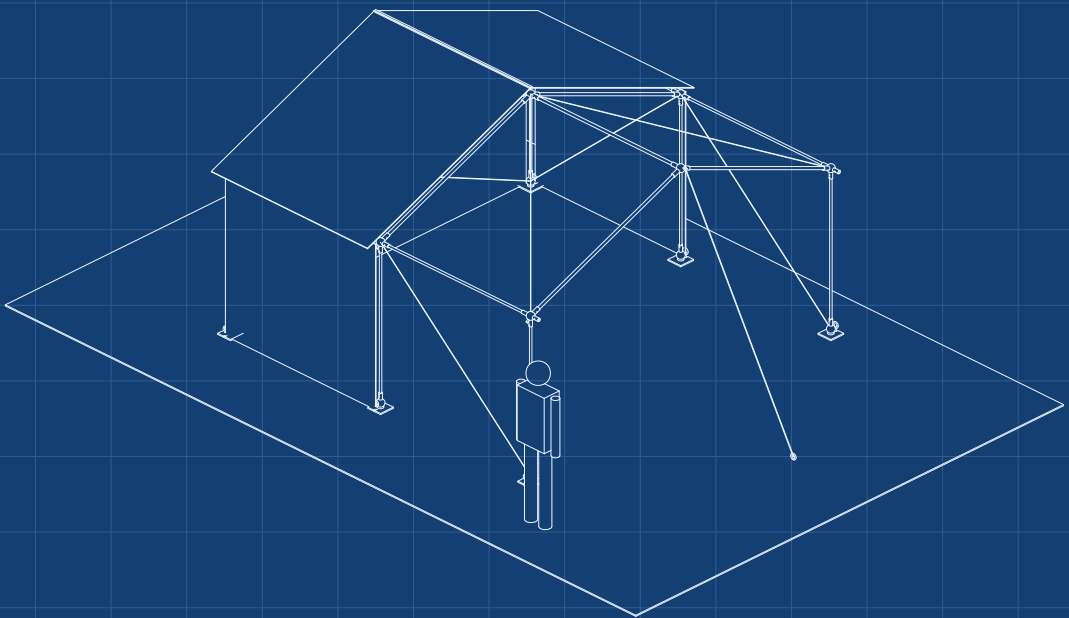

ISOMETRIC VIEW
Not to scale; grey is for scale

KEY FIGURES

Size M: 4.0 x 4.0 m floor (16 m²), eave 1.8 m, ridge 2.6 m
18 EMT members: 1 in rafters and ridge, 3/4 in posts and eaves
15 printed nodes in 4 variants, spring-button sockets, no tools
Frame kit 42.0 kg, \$443 (budget \$400); tarpaulins agency stock
Wind rating 19.7 m/s, 3/4 in post governs (SNF-CAL-001)

SNAPFRAME

Emergency shelter frame kit concept, size M

DRAWING NO. SNF-DWG-010			REV P1	SHEET 1 of 1	SIZE ANSI B
SCALE 1:100	UNITS mm	PROJECTION 	DATE 2026-09-25	DRAWN Amish Chadha	

MATERIAL / NOTES
Massing model for concept communication