



CONCEPT, NOT FOR FABRICATION


| REV | DESCRIPTION   | DATE       | BY |
|-----|---------------|------------|----|
| P1  | Concept sheet | 2026-09-25 | AC |

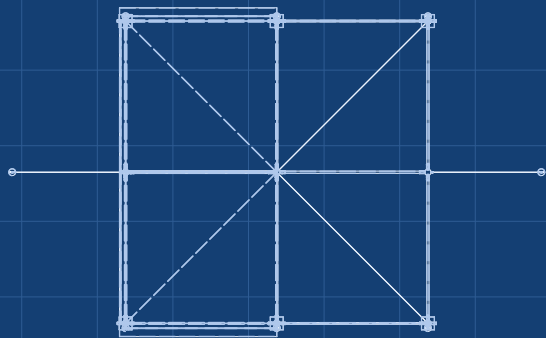


TOP VIEW  
Scale 1:100

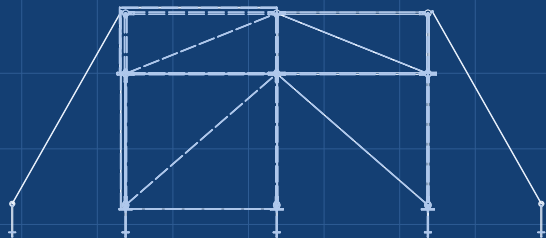

FRONT VIEW  
Scale 1:100

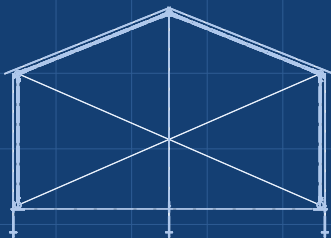

RIGHT VIEW  
Scale 1:100

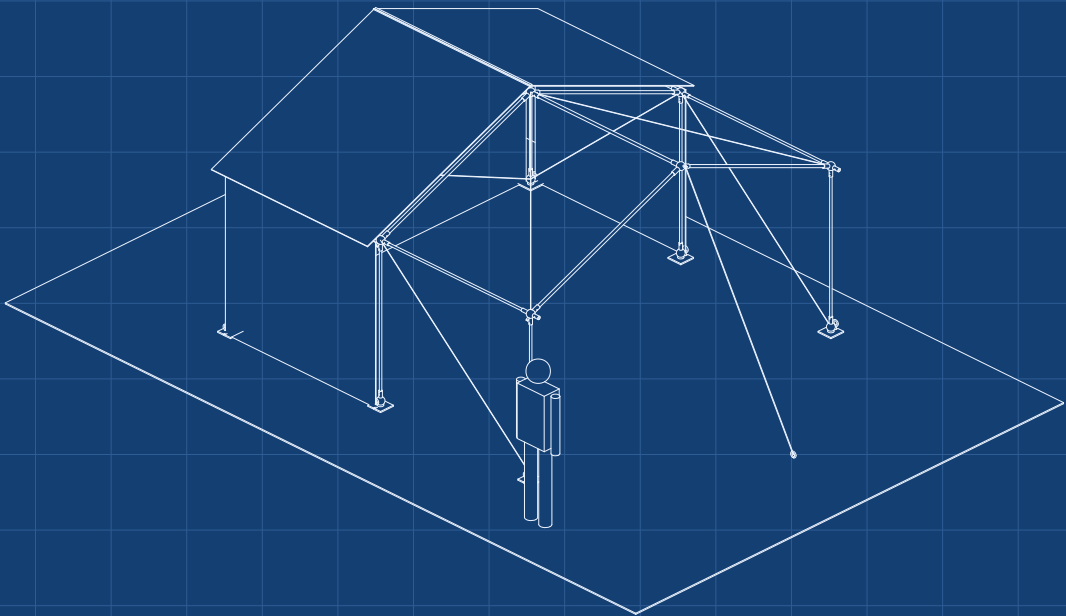

ISOMETRIC VIEW  
Not to scale; grey is for scale

KEY FIGURES

Size M: 4.0 x 4.0 m floor (16 m<sup>2</sup>), eave 1.8 m, ridge 2.6 m  
18 EMT members: 1 in rafters and ridge, 3/4 in posts and eaves  
15 printed nodes in 4 variants, spring-button sockets, no tools  
Frame kit 42.0 kg, \$443 (budget \$445); tarpaulins agency stock  
Wind rating 19.7 m/s, 3/4 in post governs (SNF-CAL-001)

SNAPFRAME

Emergency shelter frame kit concept, size M

|                                   |                    |   |                           |                              |                       |
|-----------------------------------|--------------------|---|---------------------------|------------------------------|-----------------------|
| DRAWING NO.<br><b>SNF-DWG-010</b> |                    |   | REV<br><b>P1</b>          | SHEET<br><b>1 of 1</b>       | SIZE<br><b>ANSI B</b> |
| SCALE<br><b>1:100</b>             | UNITS<br><b>mm</b> | PROJECTION<br> | DATE<br><b>2026-09-25</b> | DRAWN<br><b>Amish Chadha</b> |                       |

MATERIAL / NOTES  
Massing model for concept communication