



CONCEPT, NOT FOR FABRICATION


REV	DESCRIPTION	DATE	BY
P1	Concept sheet	2026-09-25	AC

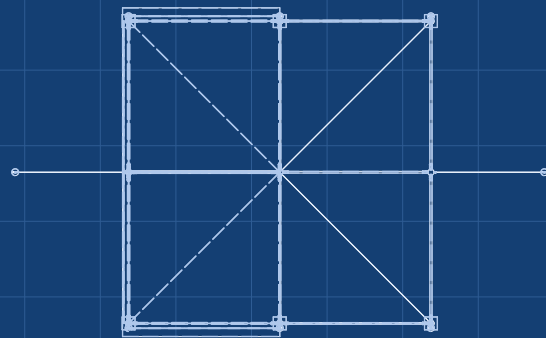


TOP VIEW
Scale 1:100

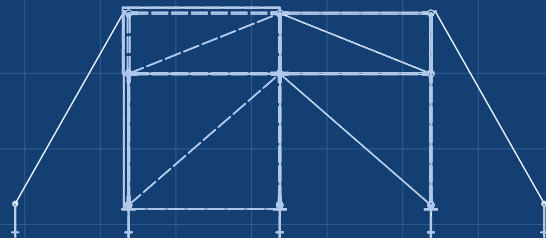

FRONT VIEW
Scale 1:100

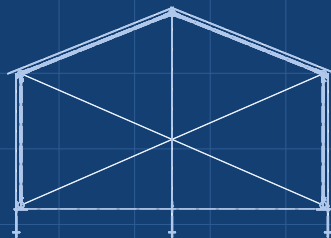

RIGHT VIEW
Scale 1:100

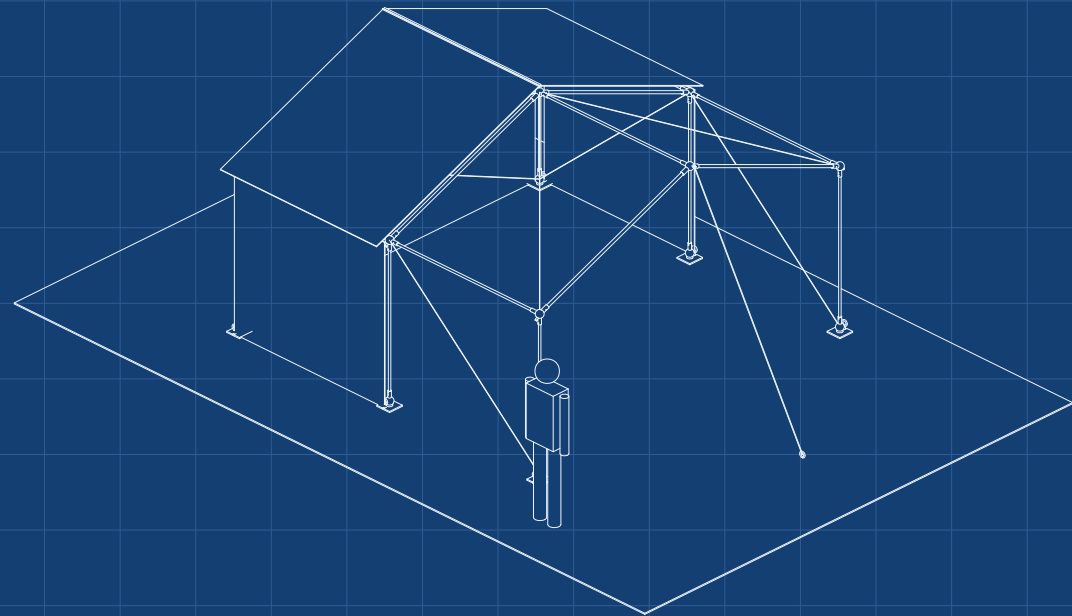

ISOMETRIC VIEW
Not to scale; grey is for scale

KEY FIGURES

Size M: 4.0 x 4.0 m floor (16 m²), eave 1.8 m, ridge 2.6 m
18 EMT members: 1 in rafters, 3/4 in elsewhere; longest 2.06 m
15 printed nodes, spring-button sockets, no tools
Frame kit 40.6 kg, \$431 (budget \$400); tarpaulins agency stock
Wind rating 17.8 m/s, ridge tube governs (SNF-CAL-001)

SNAPFRAME

Emergency shelter frame kit concept, size M

DRAWING NO. SNF-DWG-010			REV P1	SHEET 1 of 1	SIZE ANSI B
SCALE 1:100	UNITS mm	PROJECTION 	DATE 2026-09-25		DRAWN Amish Chadha
MATERIAL / NOTES Massing model for concept communication					
Licensed CERN-OHL-S-2.0 · Open Hardware Portfolio · amishchadha.com			Generated from cad/src; do not edit by hand		